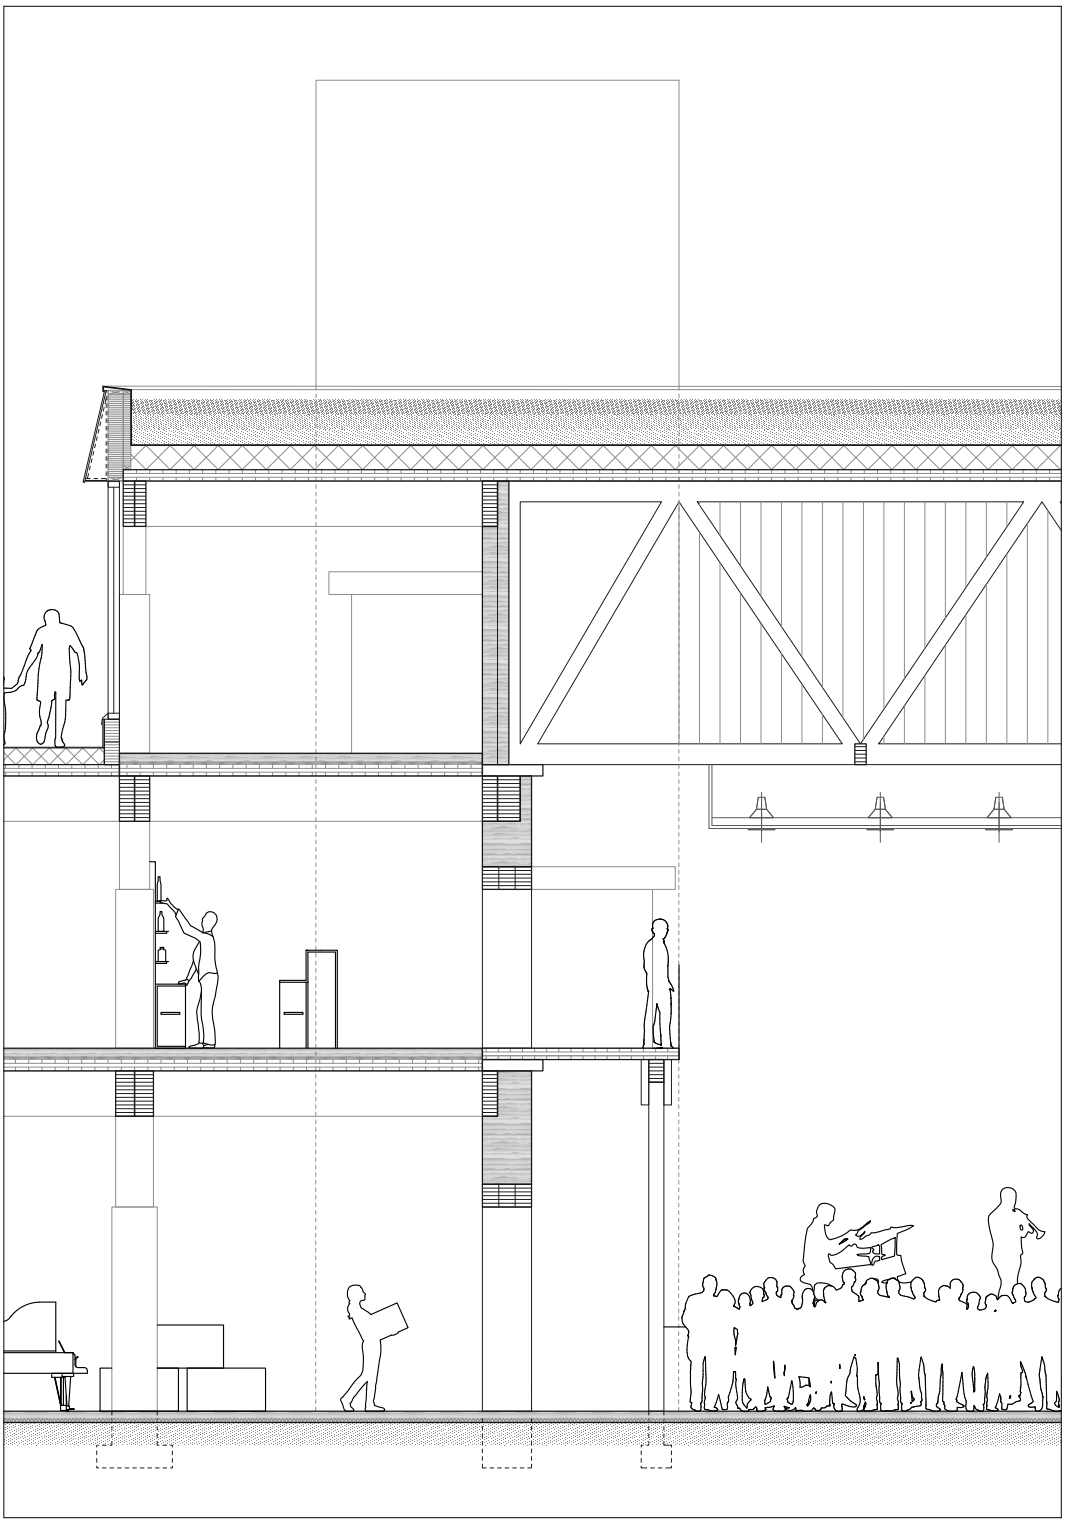


A403B MULTI-PURPOSE CENTRE