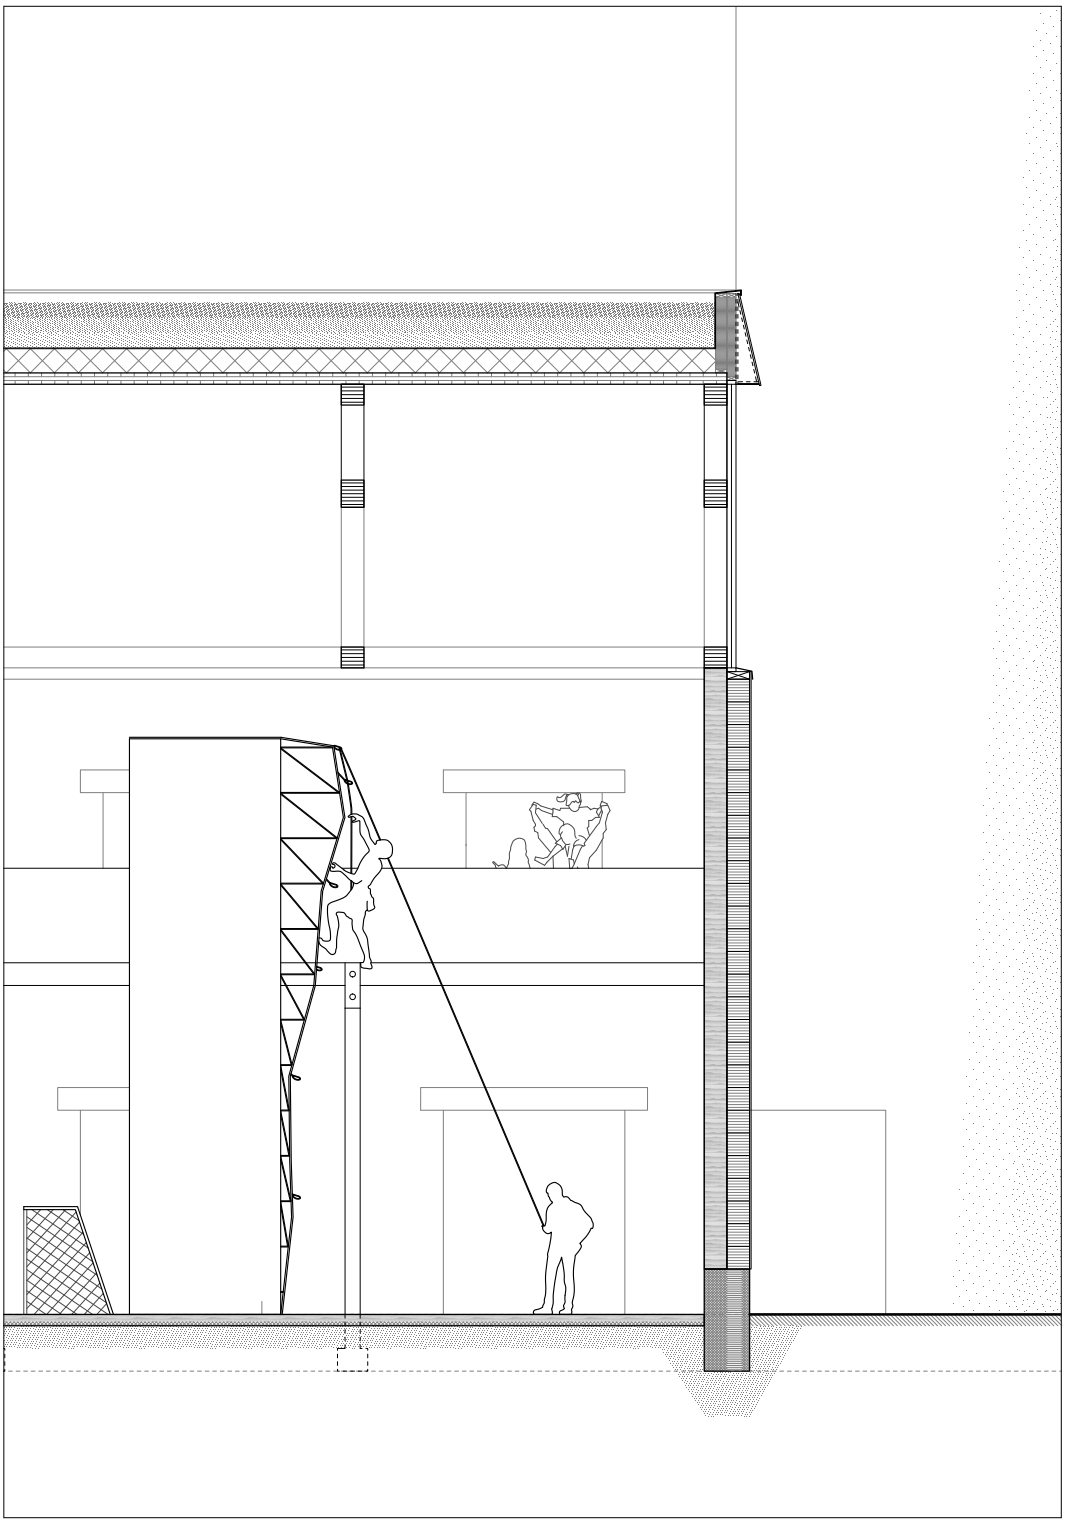


A405B MULTI-PURPOSE CENTRE